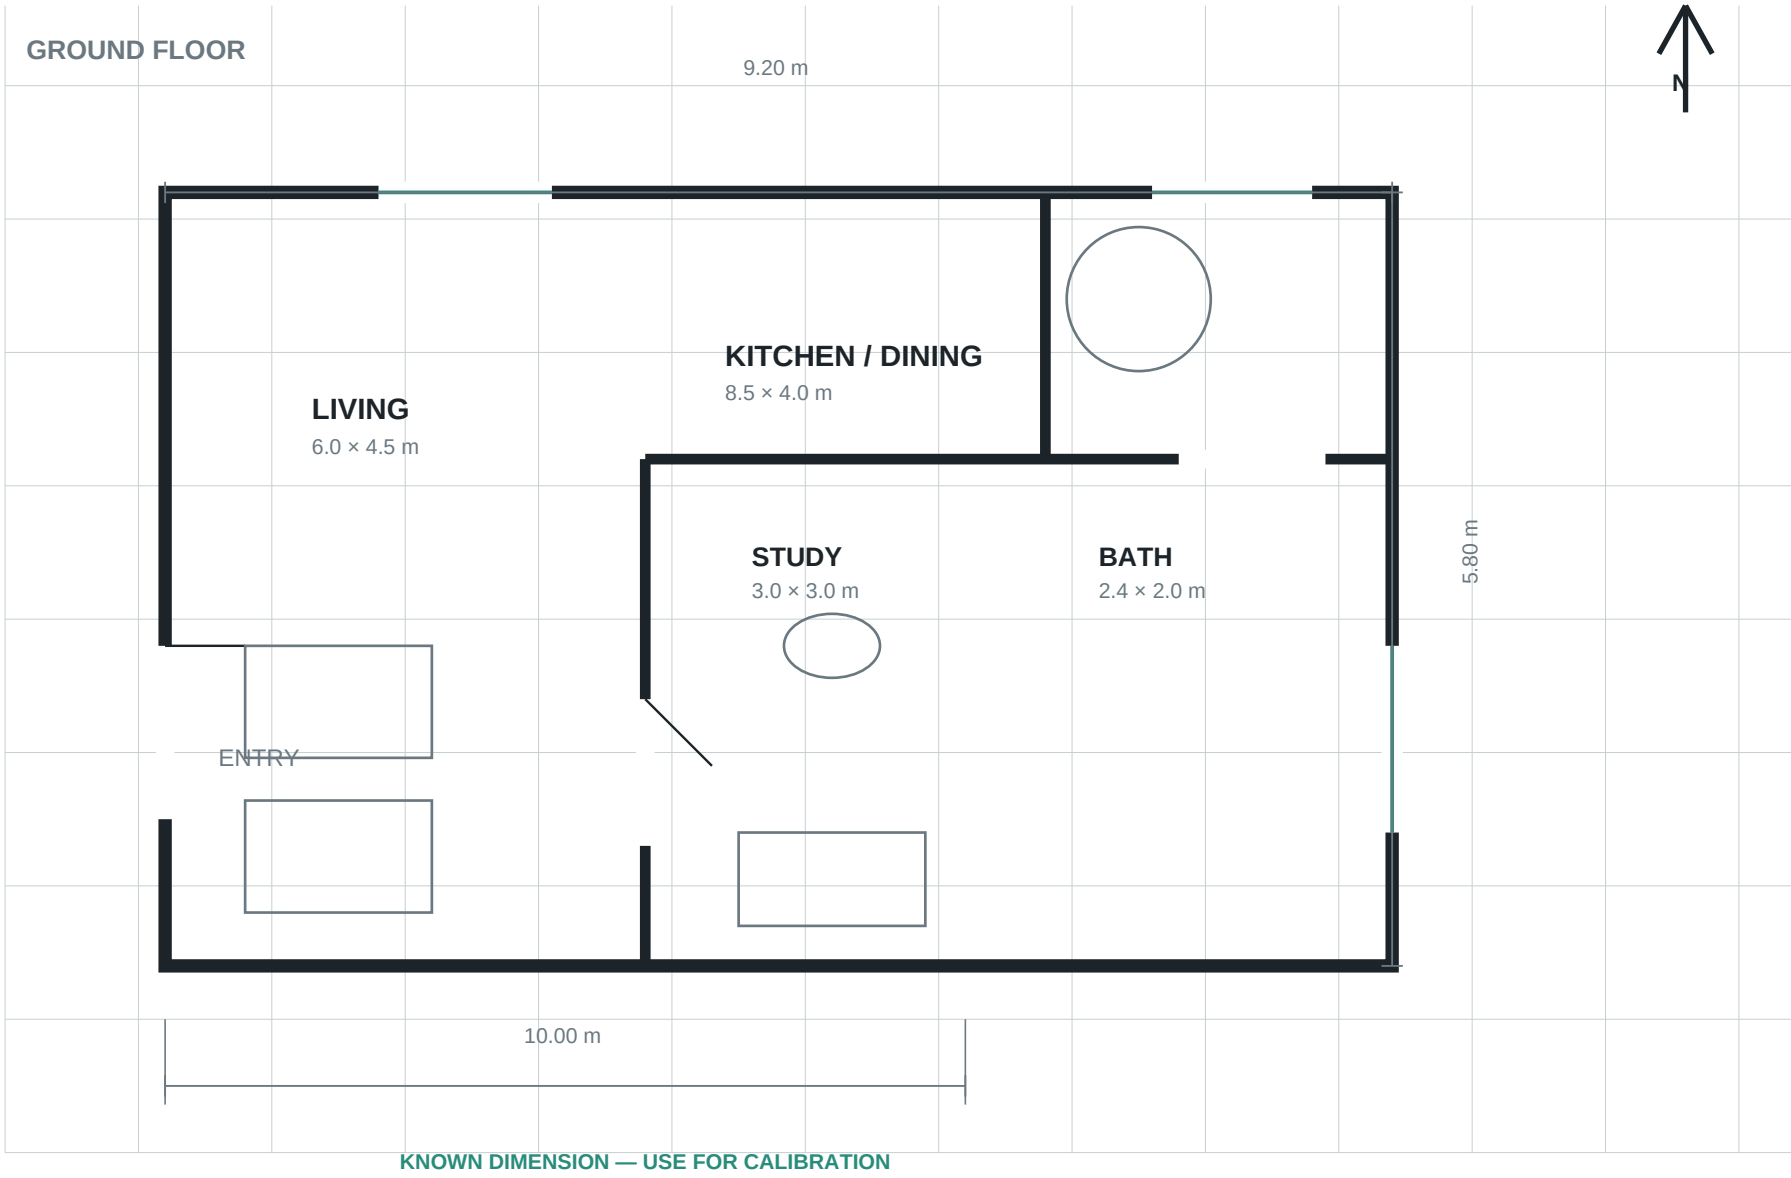

GRIDSCALR SAMPLE PROJECT

GROUND FLOOR PLAN

SHEET 1

SCALE 1:100 · DIMENSIONS IN METRES

NOT FOR CONSTRUCTION

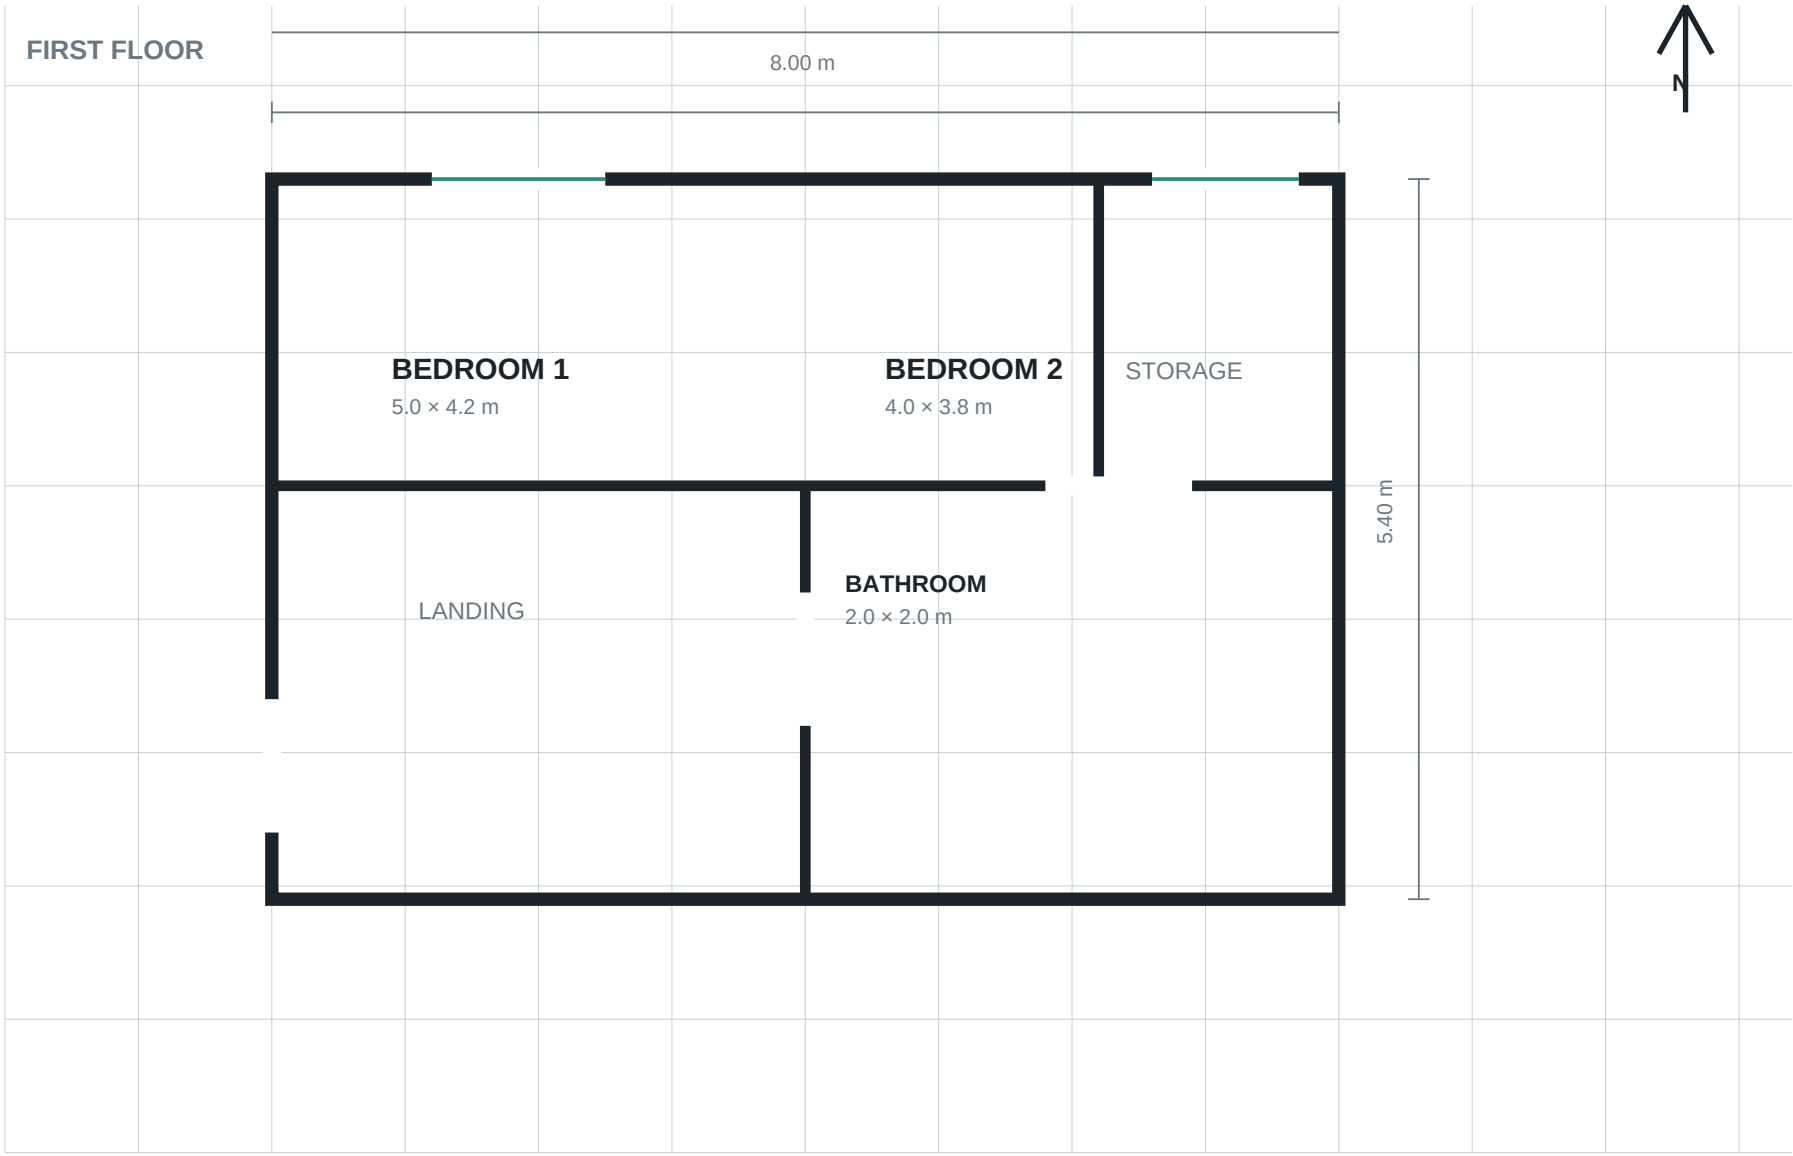

GRIDSCALR SAMPLE PROJECT

FIRST FLOOR PLAN

SHEET 2

SCALE 1:100 · DIMENSIONS IN METRES

NOT FOR CONSTRUCTION